# ПЛАН БЛІНДАЖА (ВИД ЗВЕРХУ)nЗахист від 152-мм снарядів

# БЛІНДАЖ: ВИД ЗВЕРХУ (УКР)

БЛІНДАЖ: ВИД ЗВЕРХУ

## ПОСИЛЕНИЙ БЛІНДАЖ (КЛАС ЗАХИСТУ: ВАЖКА АРТА)nПерекриття: 3-4 шари колод + 2м грунту

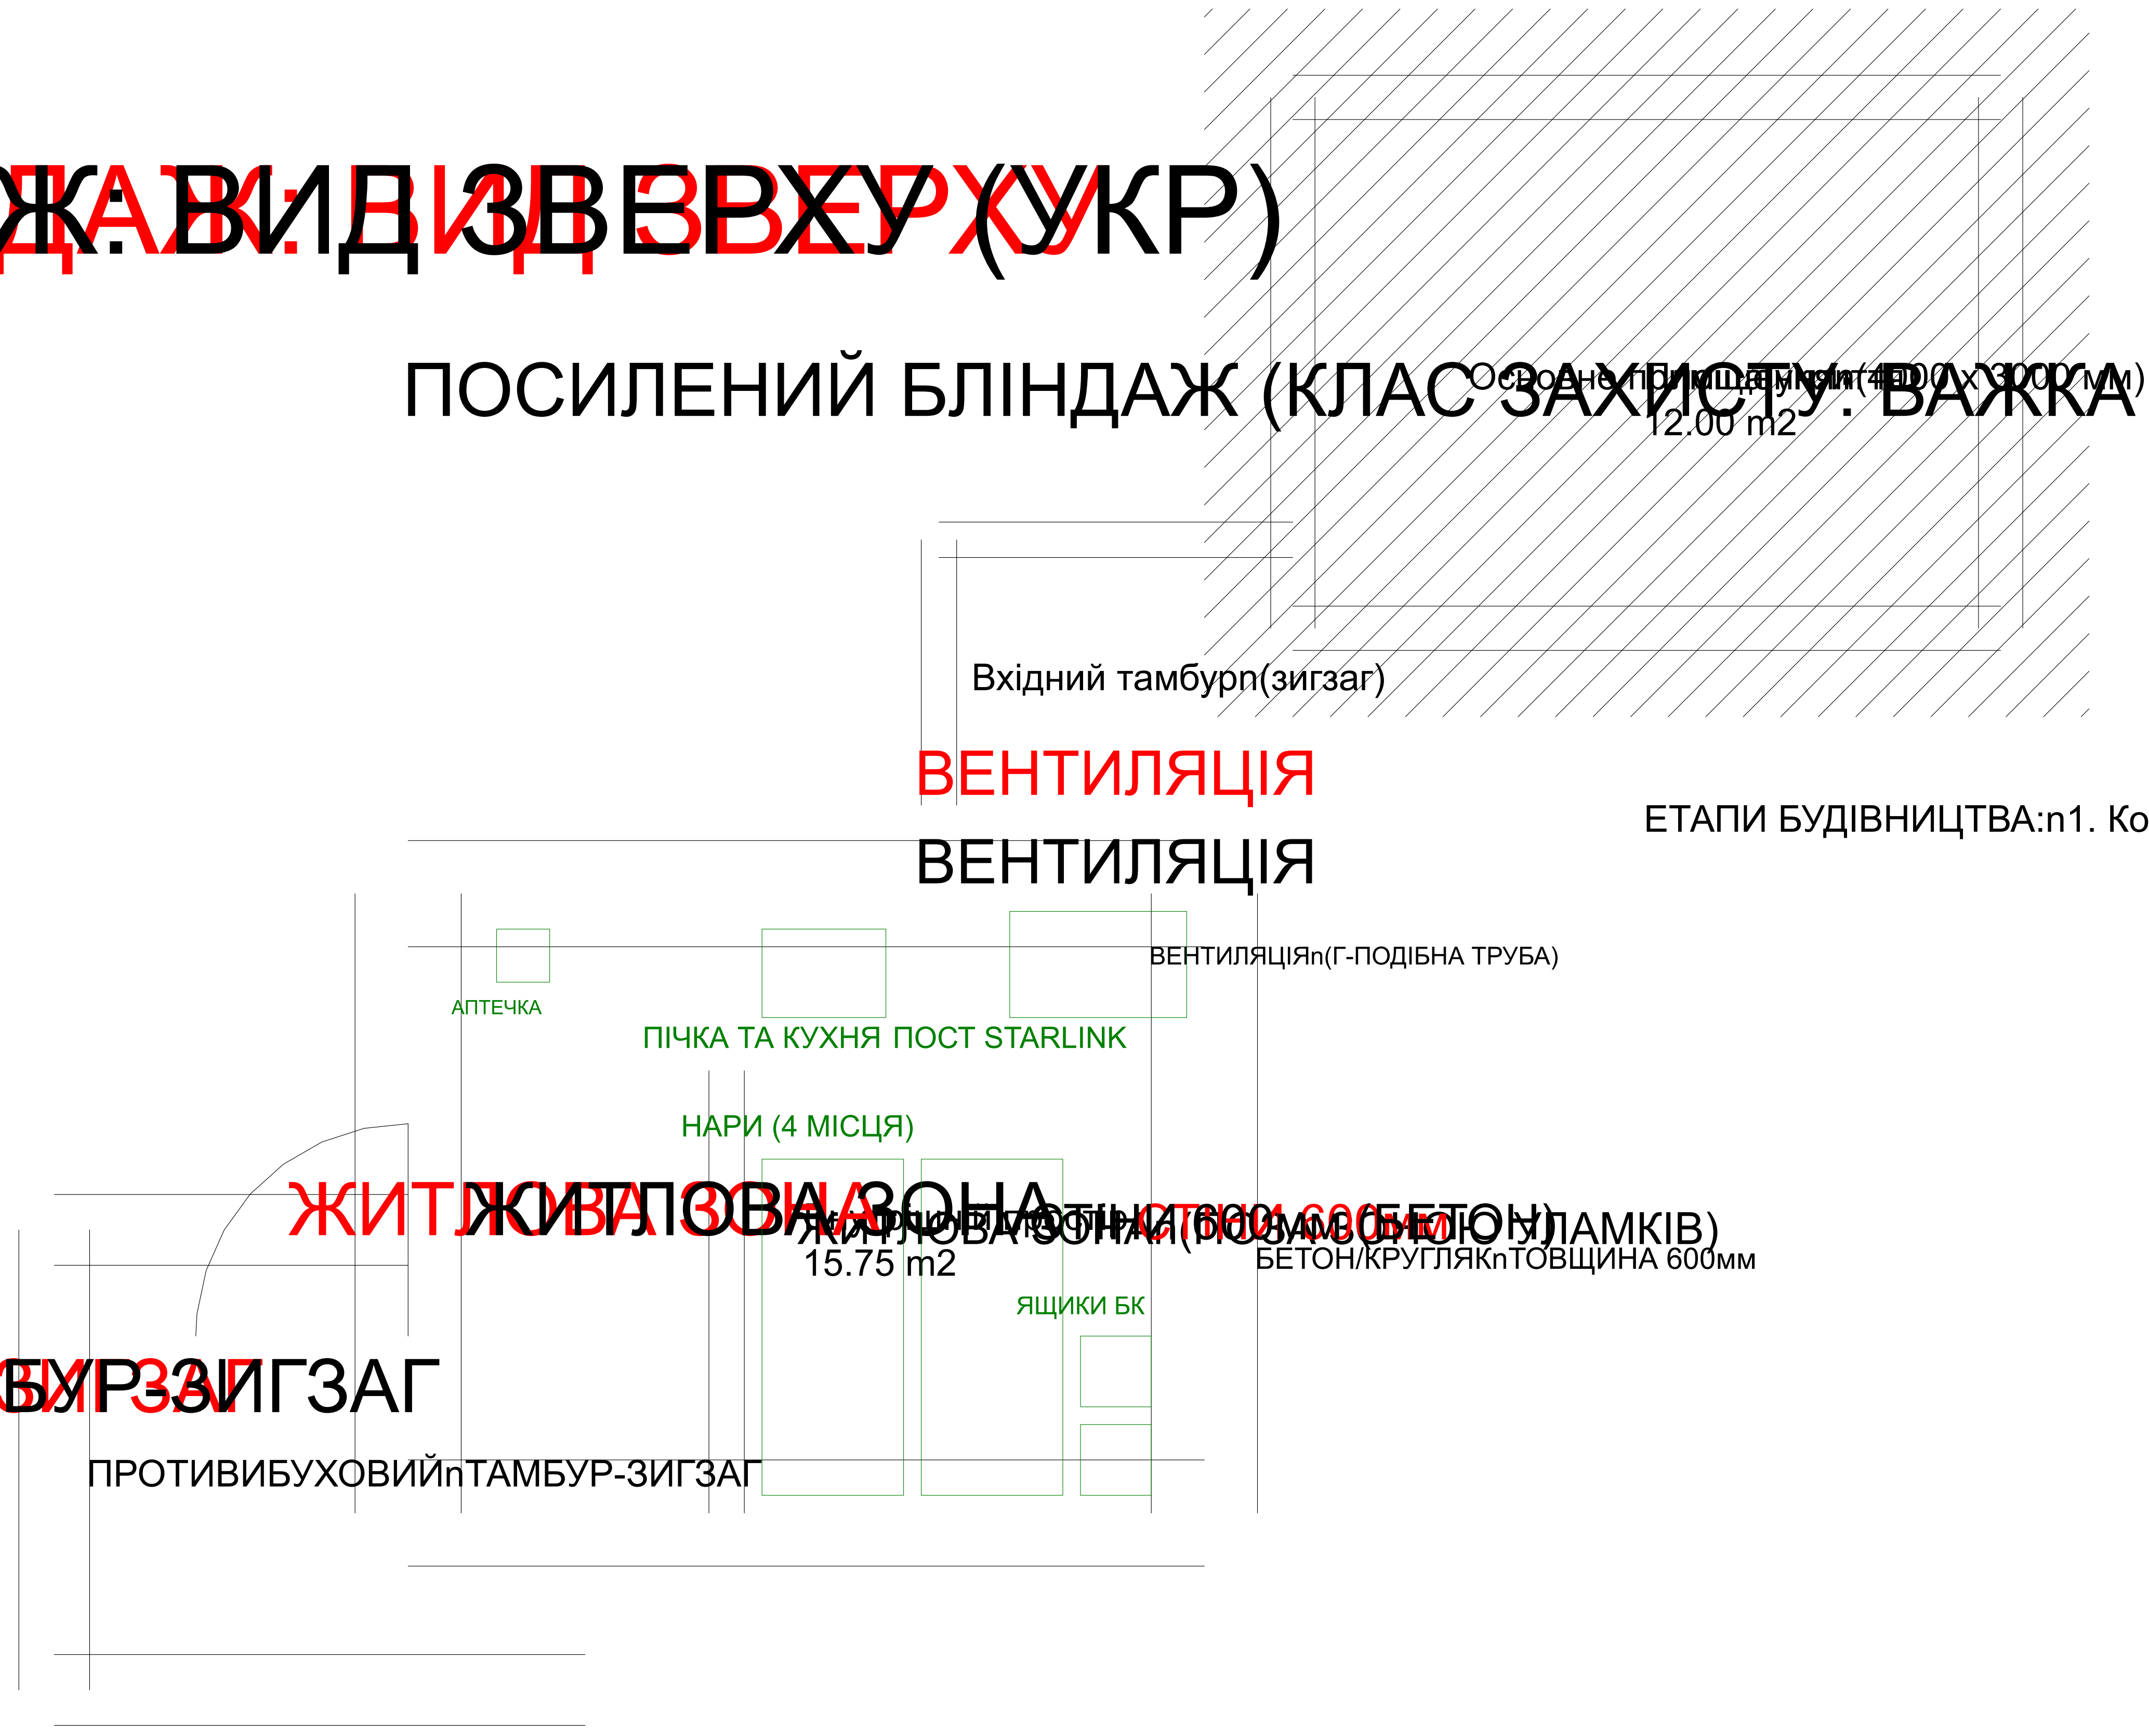
Основне приміщення(4000 x 3000 мм)
12.00 m2
Вхідний тамбурn(зигзаг)
ВЕНТИЛЯЦІЯ
ВЕНТИЛЯЦІЯ
ВЕНТИЛЯЦІЯn(Г-ПОДІБНА ТРУБА)
АПТЕЧКА
ПІЧКА ТА КУХНЯ
ПОСТ STARLINK
НАРИ (4 МІСЦЯ)
ЖИТЛОВА ЗОНА
ЖИТЛОВА ЗОНА
ЖИТЛОВА ЗОНАn(ПОЗА ЗОНОЮ УЛАМКІВ)
15.75 m2
СТІНИ 600мм
БЕТОН/КРУГЛЯКnТОВЩИНА 600мм
ЯЩИКИ БК
ТАМБУР-ЗИГЗАГ
ТАМБУР-ЗИГЗАГ
ПРОТИВИБУХОВИЙnТАМБУР-ЗИГЗАГ

ЕТАПИ БУДІВНИЦТВА:n1. Котлован (глибина 3.5-4м)n2. Дренаж та підлогаn3. Стіни (кругляк/бетон)n4. Внутрішня перегородкаn5. Перекриття (3-4 шари колод)n6. Гідроізоляція та земля (2м)

БЕРМА ТА ВОДОВІДВІДn(ЗАХИСТ ВІД ЗАТОПЛЕННЯ)